

ГРПШ МПГ - РЕД-6-25х65-Н - 600(0,3-н.д.) - 2-ОЭ-0-Т-ПГ.0

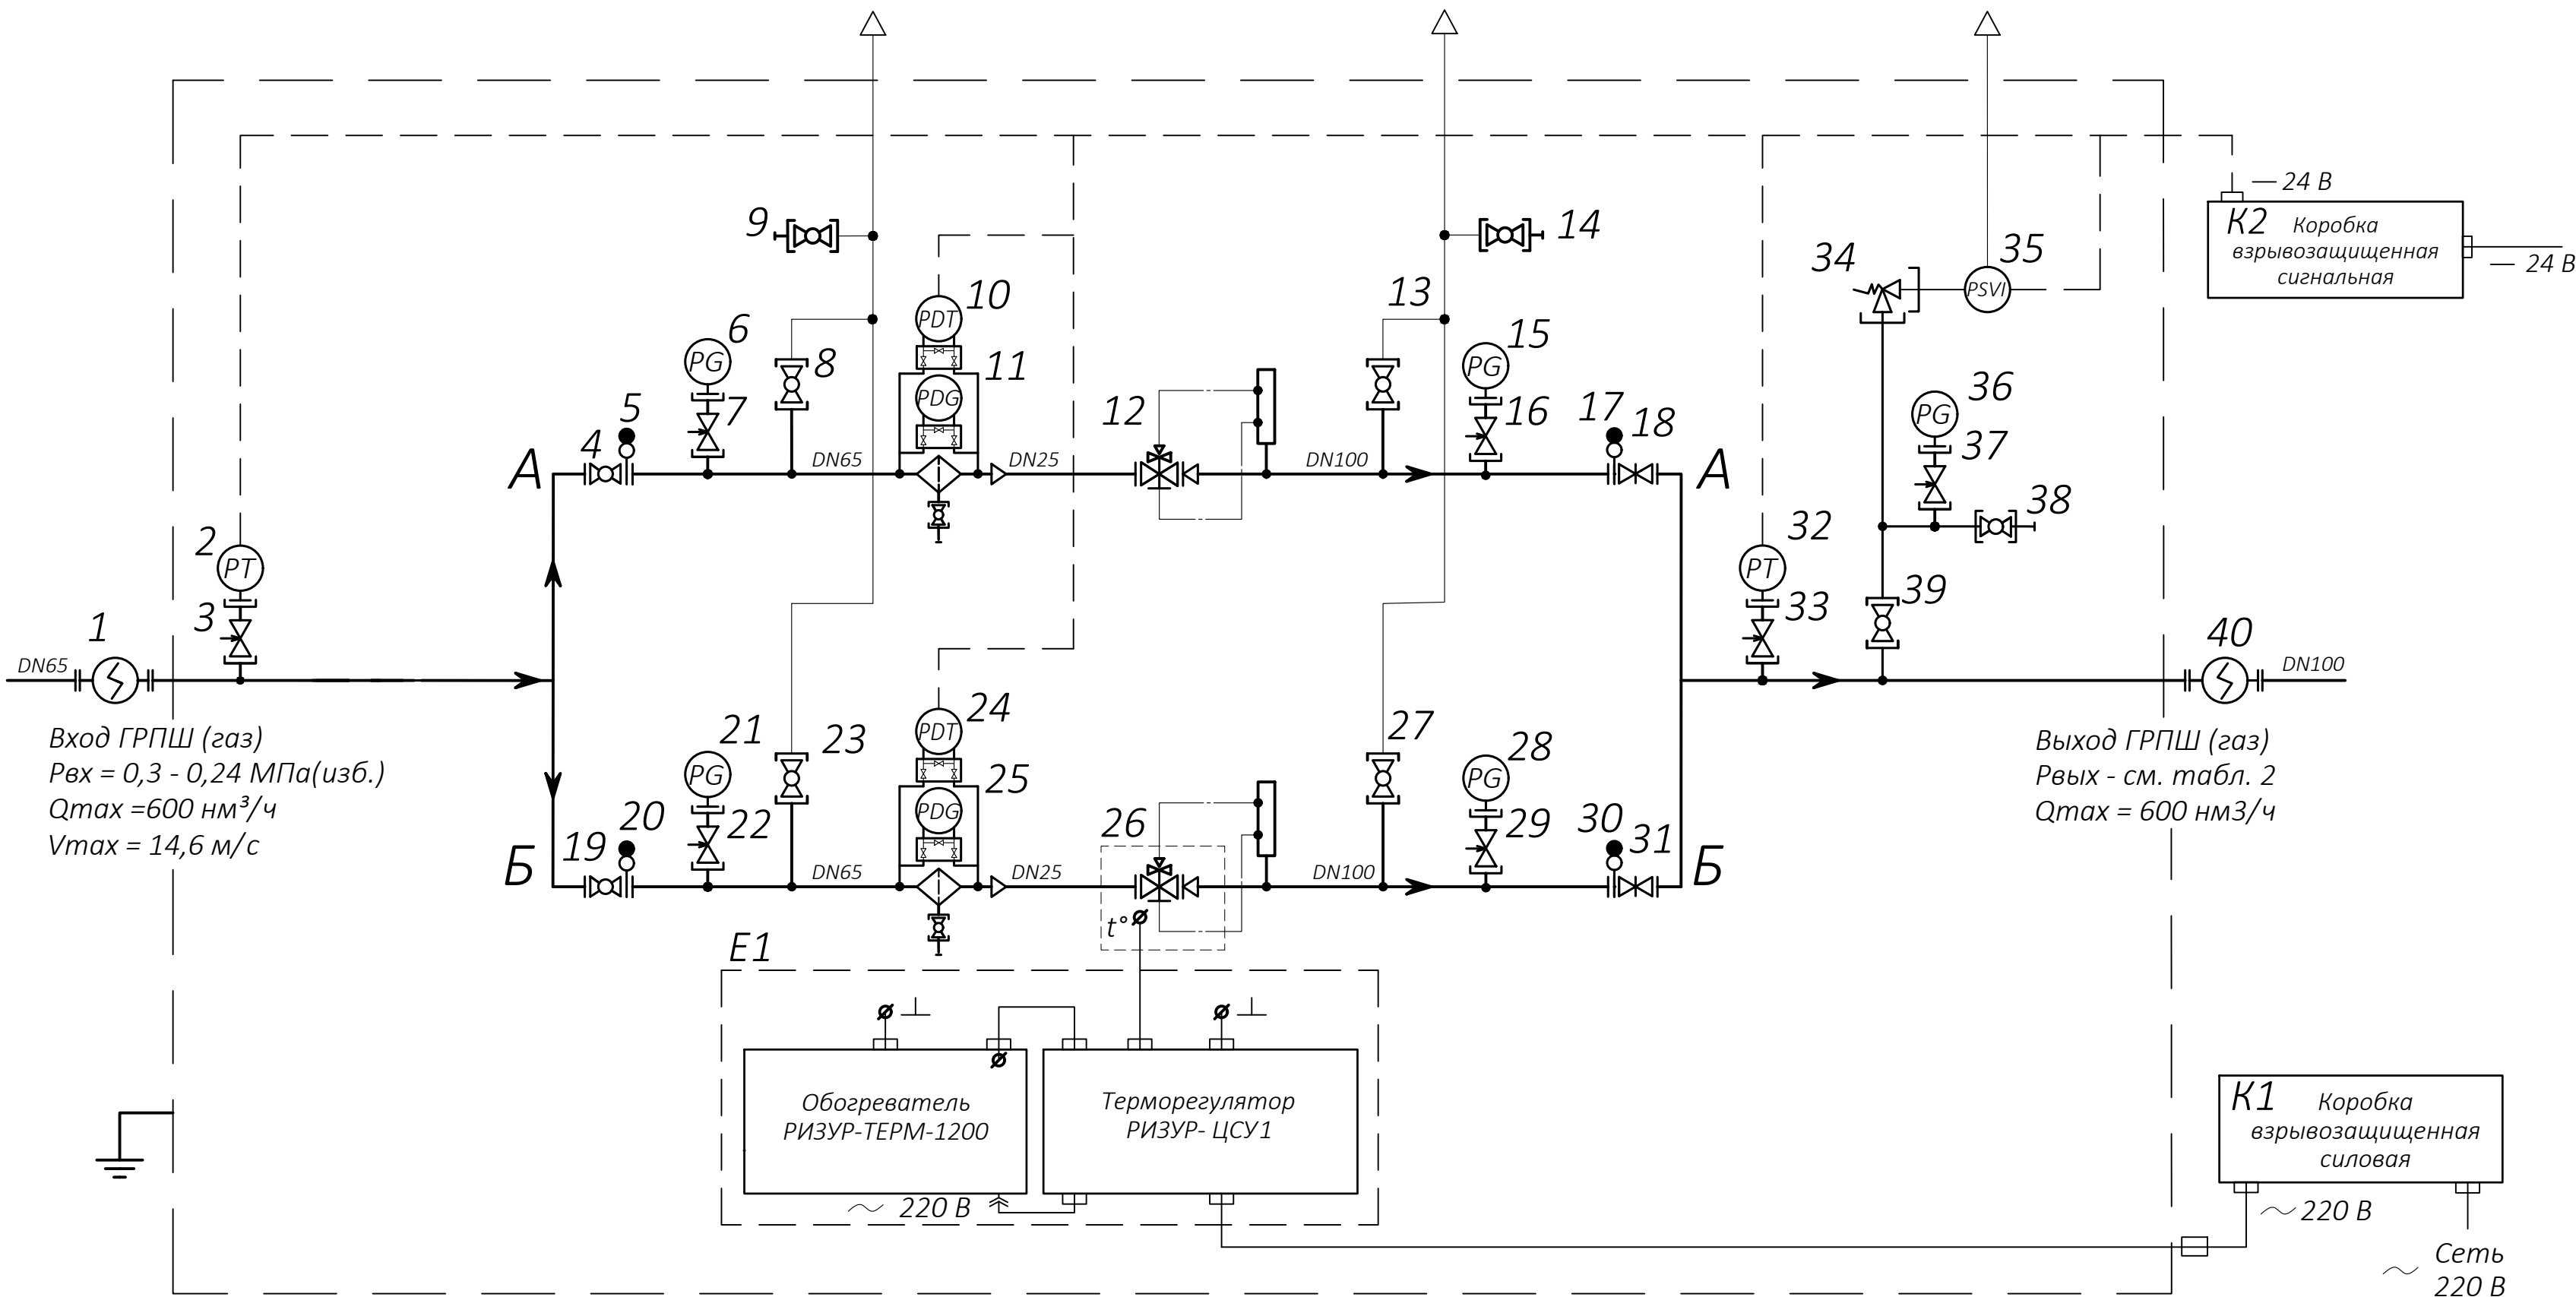


Таблица 1

Обозначение	Наименование	№ п/п	Обозначение	Наименование	№ п/п	Обозначение	Наименование	№ п/п
→	Направление движения рабочей среды	—	⎓	Вставка электроизолирующая	1,40	Ⓜ	Датчик перепада давления	10,24
—	Патрубок со съёмной заглушкой	—	Ⓜ	Датчик давления	2,32	Ⓜ	Фильтр газовый с указателем перепада давления с дренажным краном	11,25
+	Пересечение газопроводов без соединения	—	Ⓜ	Клапан под манометр	3,7,16,22,29,33,37	Ⓜ	Регулятор давления газа со встроенным ПЗК	12,26
↗	Переход на большее сечение трубопровода	—	Ⓜ	Кран шаровой	4,8,9,13,14,19,23,29,38,39	Ⓜ	Затвор дисковый поворотный	18,31
↑	Продувочная свеча	—	Ⓜ	Заглушка фланцевая поворотная	5,17,20,30	Ⓜ	Клапан предохранительный сбросной (ПСК)	34
+	Соединение трубопроводов	—	Ⓜ	Манометр	6,15,21,28,36	Ⓜ	Датчик срабатывания ПСК	35
—E	Соединение муфтовое	—						
—	Соединение фланцевое	—						
—	Трубопровод основной	—						
—	Трубопровод сбросной	—						

Таблица 2

№	Рвых, МПа (изб.)	Vmax, м/с
1	0,0018	20,19
2	0,0017	20,21
3	0,0016	20,23
4	0,0015	20,25

Изм.	Лист	№ докум.	Подп.	Дата	ДПМА.067327.082-044С3	Лит.	Масса	Масштаб
Разраб.	Григорьева							
Пров.	Рыбалко							
Н. контр.								
Утв.	Гончаров				Пункт газорегуляторный шкафной (ГРПШ)	Лист	Листов 1	
					Схема комбинированная			