

ДПМА.067327.266Х3

ГРПБ МПГ-РЕД-8-150-В-10000(0,3-0,087)/РЕД-6-50-Н-1100(0,3-н.д.)-4-ОЭ-0.Т

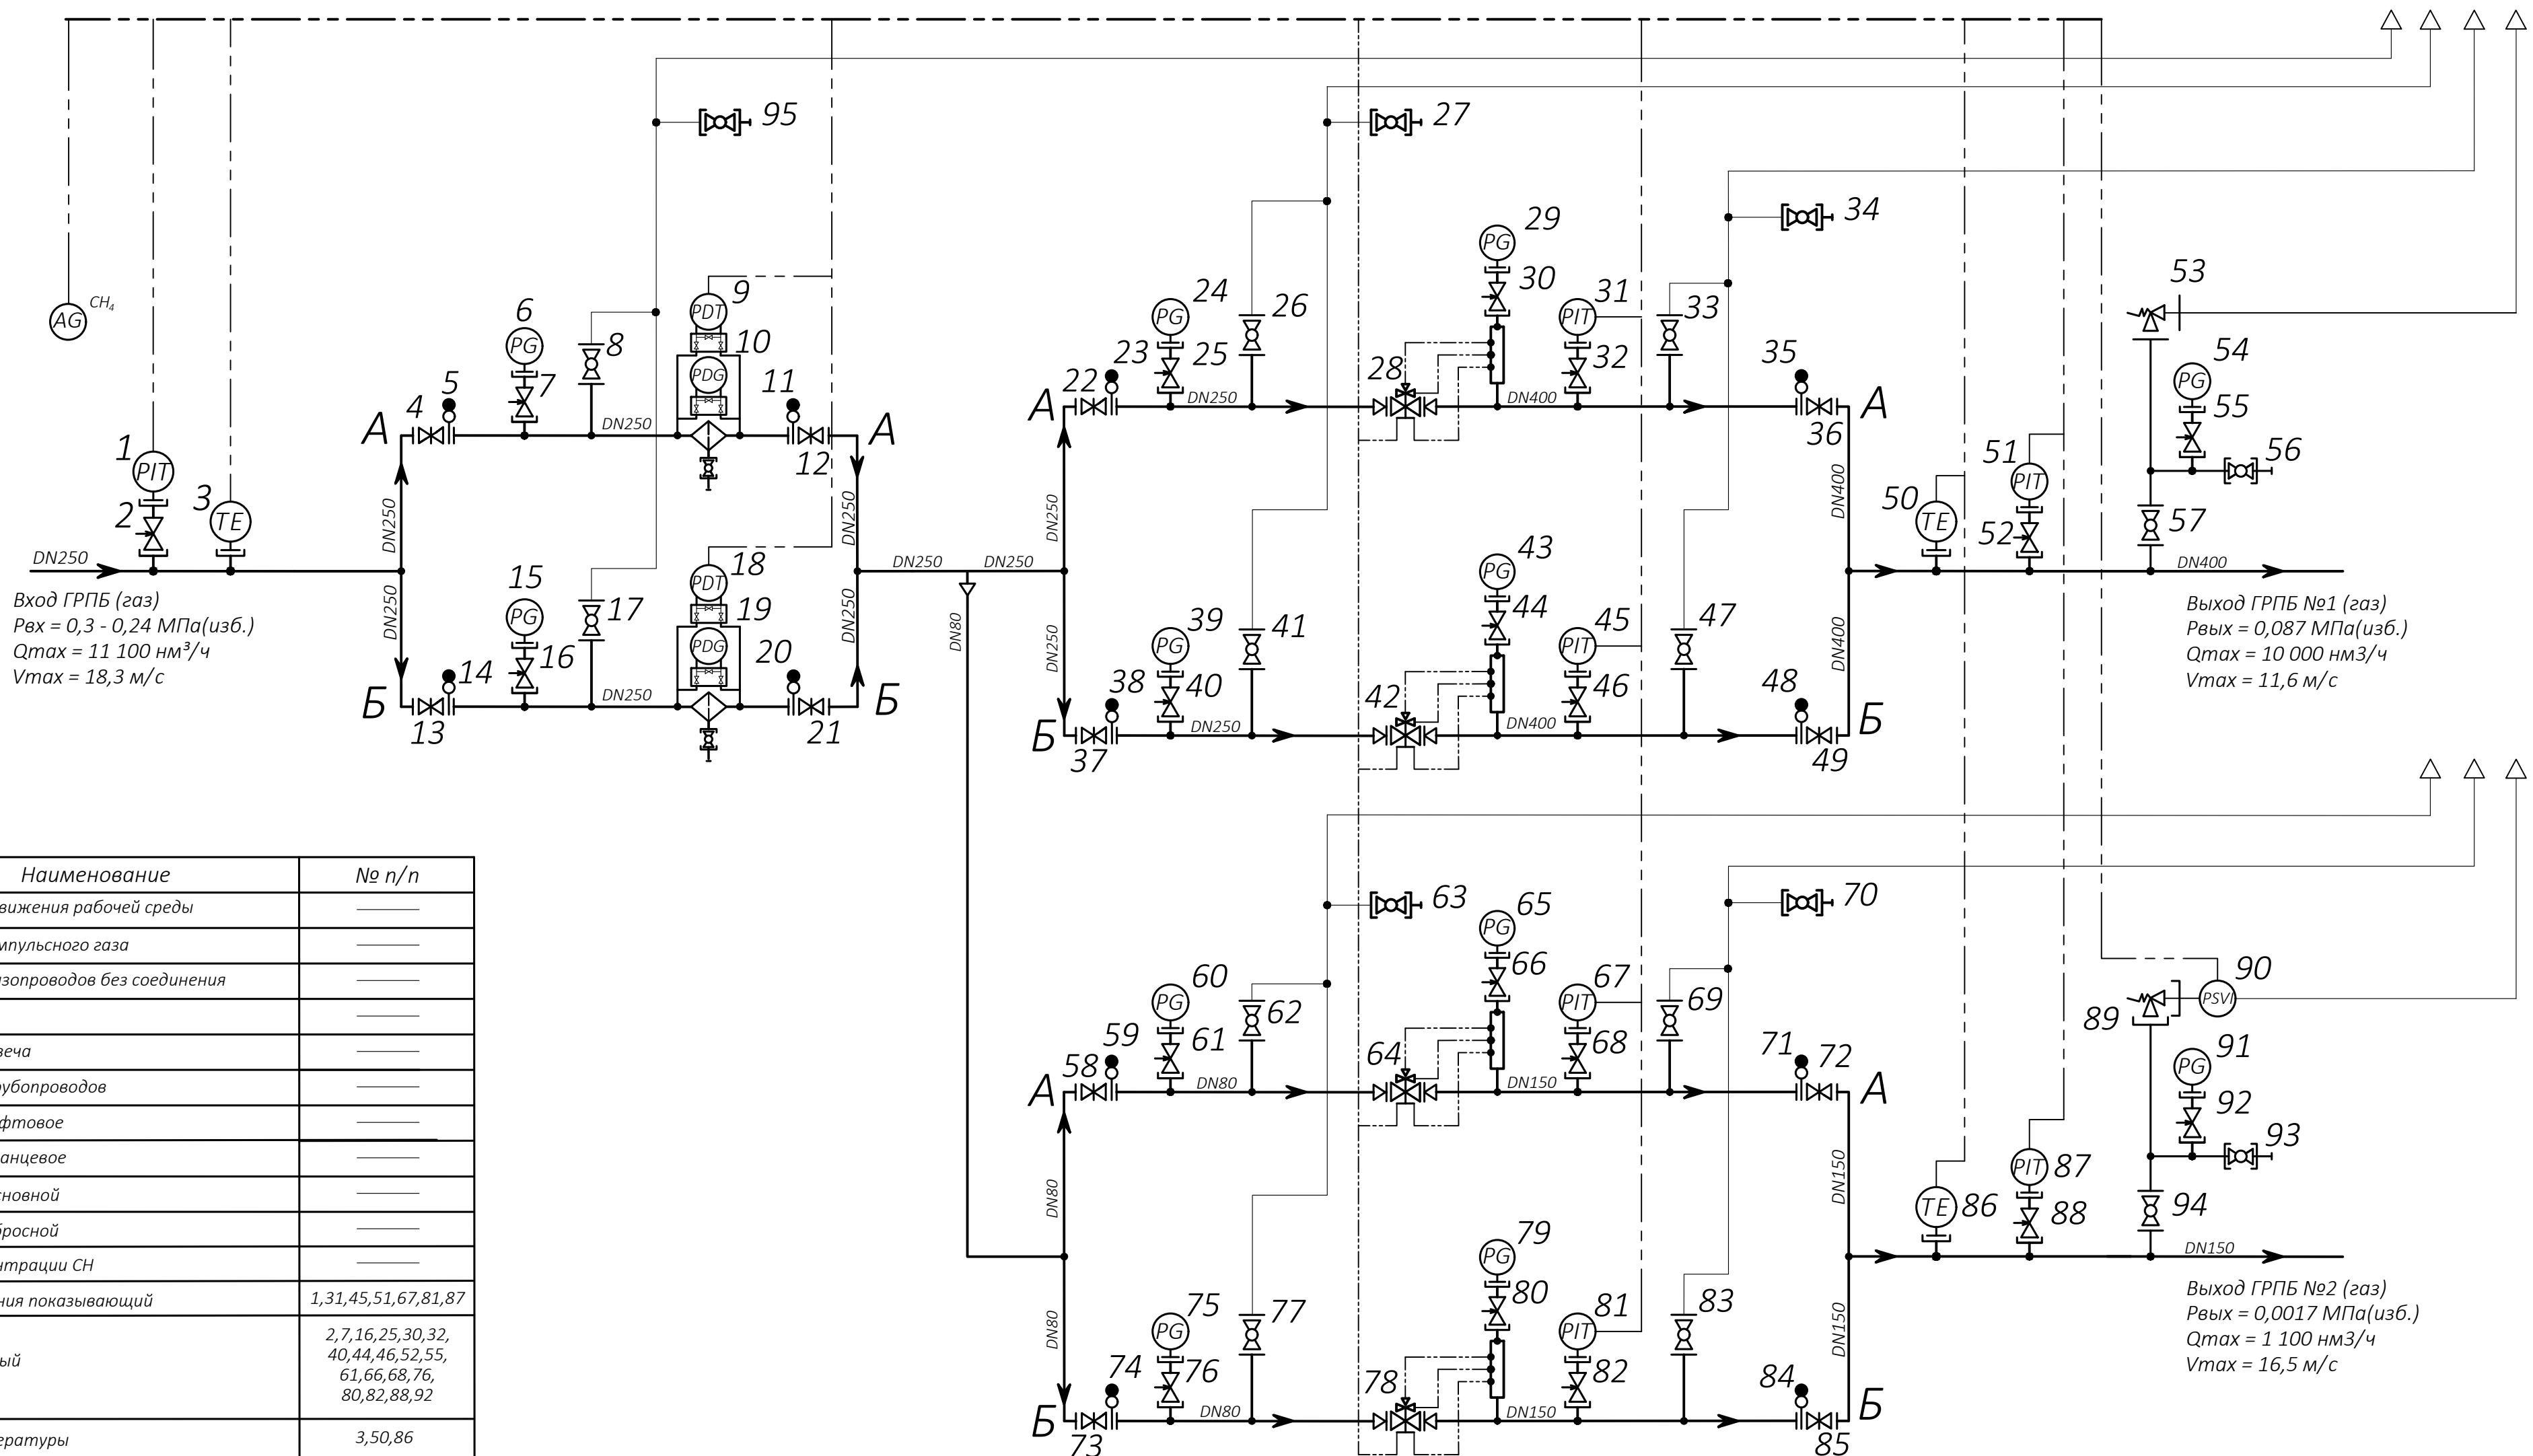
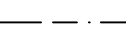
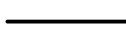
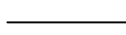


Таблица 1

Обозначение	Наименование	№ п/п
	Направление движения рабочей среды	—
	Трубопровод импульсного газа	—
	Пересечение газопроводов без соединения	—
	Переход	—
	Продувочная свеча	—
	Соединение трубопроводов	—
	Соединение муфтовое	—
	Соединение фланцевое	—
	Трубопровод основной	—
	Трубопровод сбросной	—
	Датчик концентрации CH ₄	—
	Датчик давления показывающий	1,31,45,51,67,81,87
	Клапан запорный	2,7,16,25,30,32, 40,44,46,52,55, 61,66,68,76, 80,82,88,92
	Датчик температуры	3,50,86
	Кран шаровой	8,17,26,27,33,34, 41,47,56,57,62,63, 69,70,77,83,93,94,95
	Заглушка поворотная	5,11,14,20,23,35, 38,48,59,71,74,84
	Манометр	6,15,24,29,39,43, 54,60,65,75,79,91
	Датчик перепада давления	9,18
	Фильтр газовый с указателем перепада давления и дренажным краном	10,19
	Затвор дисковый поворотный	4,12,13,21,22,36, 37,49,58,72,73,85
	Регулятор давления со встроенным ПЗК	28,42,64,78
	Клапан предохранительный сбросной (ПСК)	53,89
	Датчик срабатывания ПСК	90

						ДПМА.067327.266Х3					
						Пункт газорегуляторный блочный (ГРПБ)			Лит.	Масса	Масштаб
Изм.	Лист	№ докум.	Подп.	Дата						-	-
Разраб.	Григорьева										
Пров.	Денисов										
						Схема газовая			Лист	Листов 1	
Н. контр.										МОСПРОМГАЗ Разработка. Производство. Обслуживание.	
Утв.	Гончаров										