


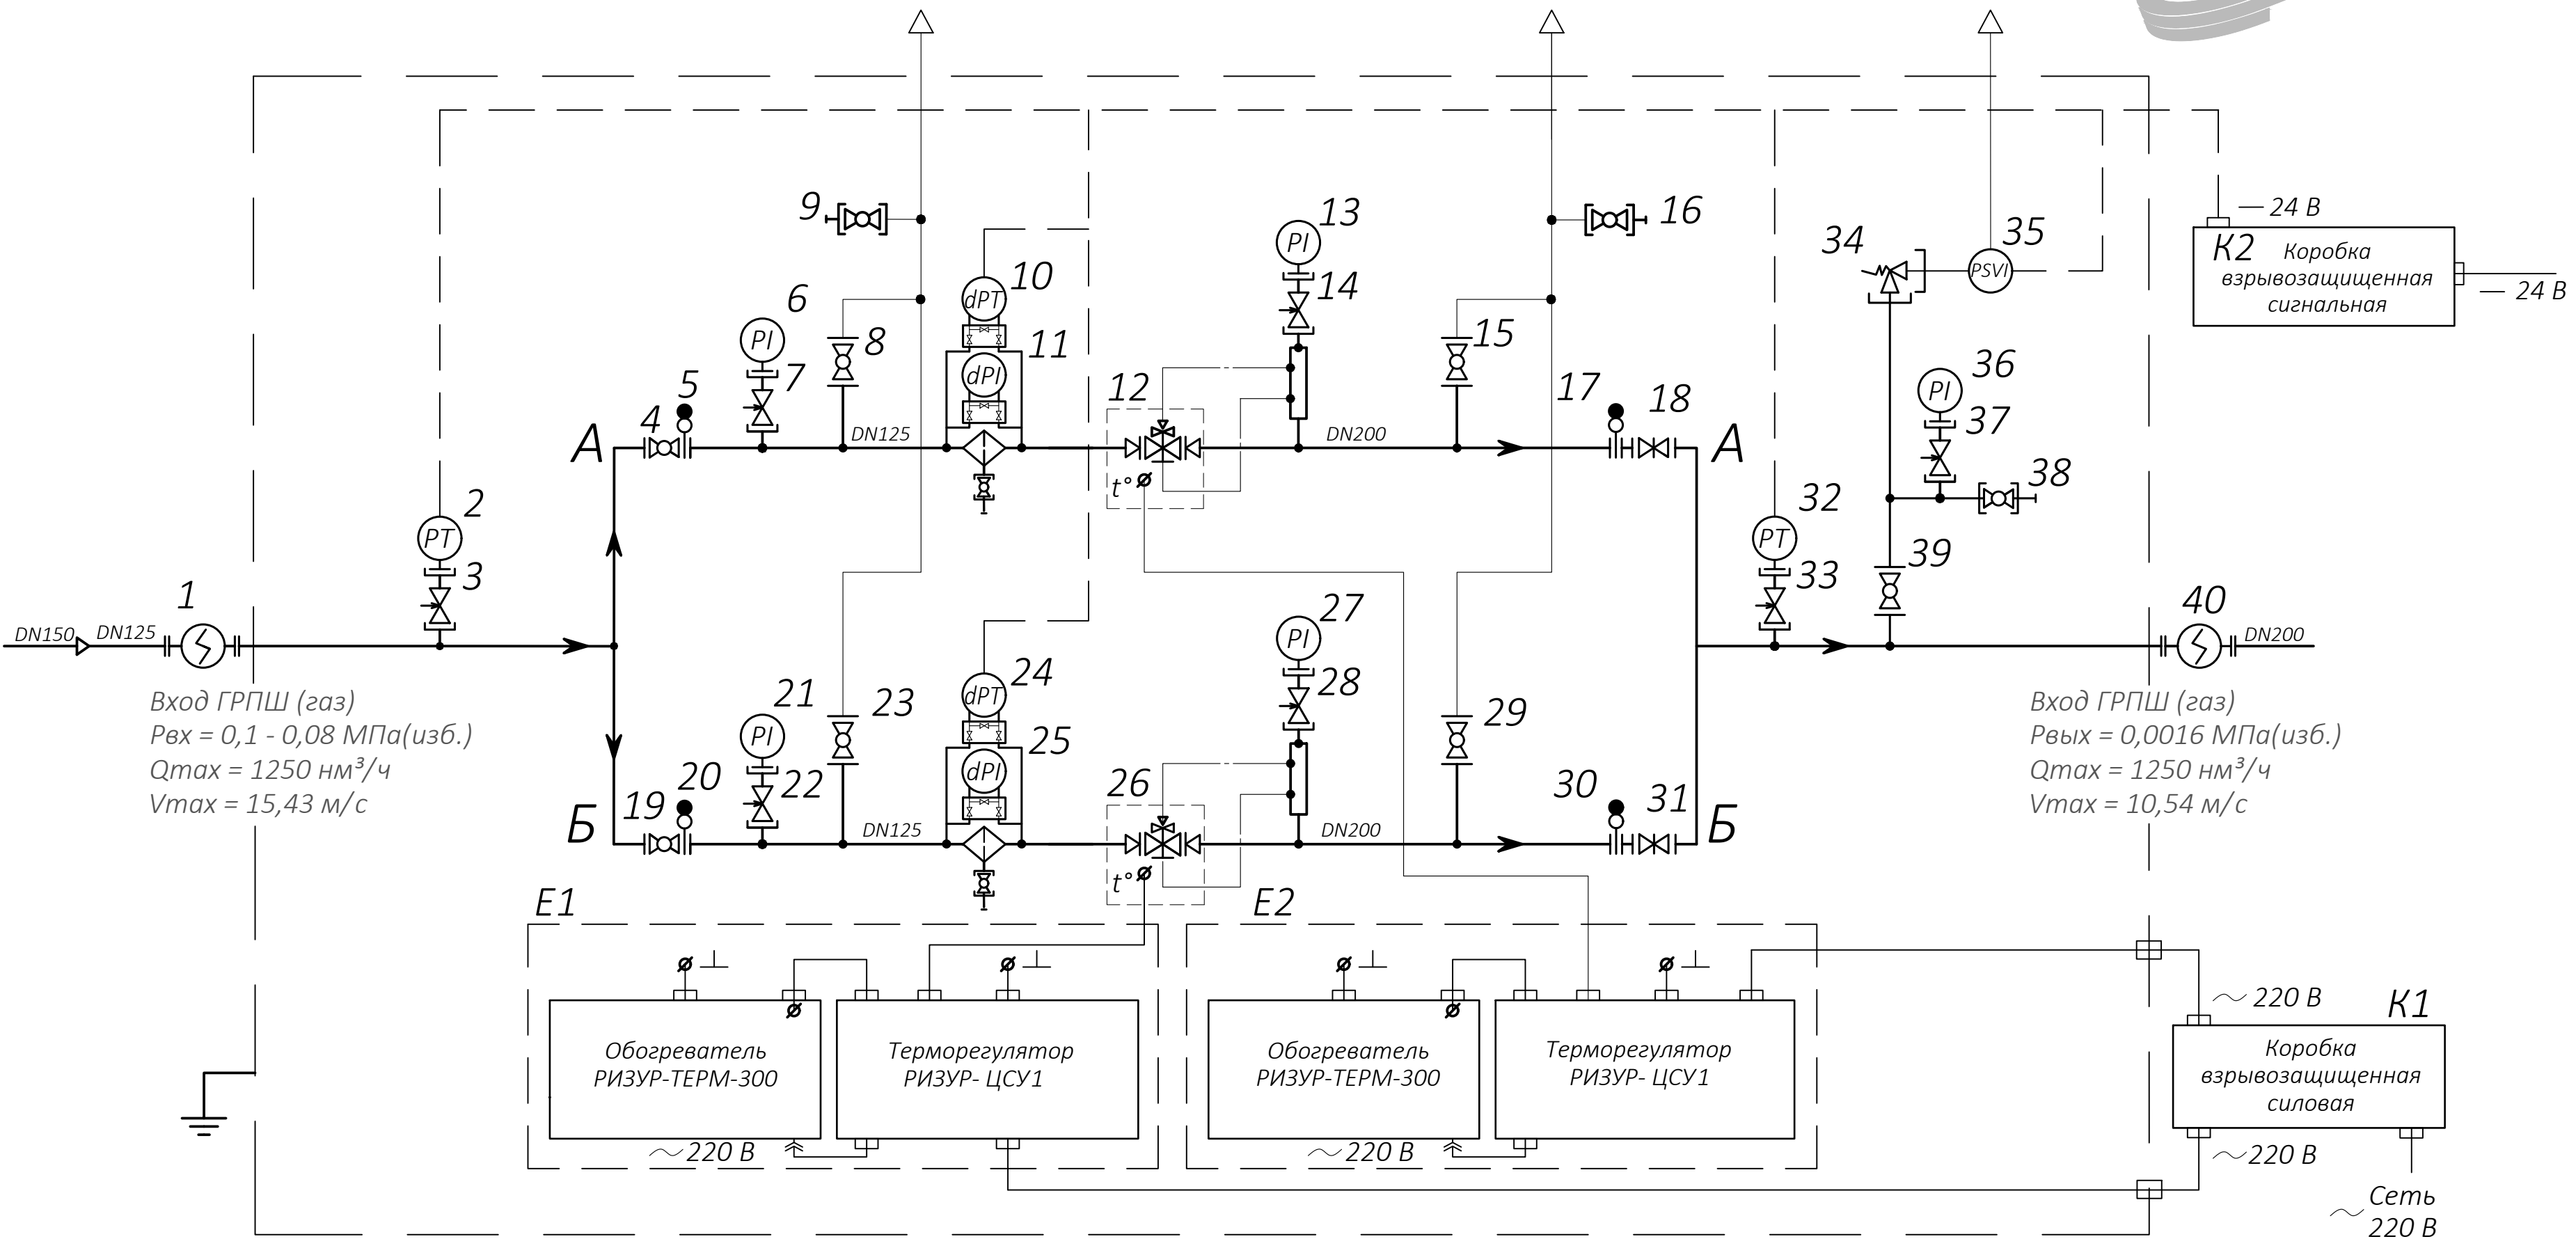

Обозначение	Наименование	№ п/п	Обозначение	Наименование	№ п/п	Обозначение	Наименование	№ п/п
→	Направление движения рабочей среды	—	— —	Вставка электроизолирующая	1,40	Ⓟ	Датчик перепада давления	10,24
—	Патрубок со съёмной заглушкой	—	Ⓟ	Датчик давления	2,32	Ⓟ	Фильтр газовый с указателем перепада давления	11,25
—+	Пересечение газопроводов без соединения	—	Ⓟ	Клапан запорный игольчатый	3,7,14,22,28,33,37	Ⓟ	Регулятор давления со встроенным ПЗК	12,26
—Ⓟ	Переход на большее сечение трубопровода	—	Ⓟ	Кран шаровой	4,8,9,15,16,19,23,29,38,39	Ⓟ	Клапан предохранительный сбросной (ПСК)	34
Ⓟ	Продувочная свеча	—	Ⓟ	Заглушка фланцевая поворотная	5,17,20,30	Ⓟ	Датчик срабатывания ПСК	35
—+	Соединение трубопроводов	—	Ⓟ	Манометр	6,13,21,27,36			
—E—	Соединение муфтовое	—						
— —	Соединение фланцевое	—						
—	Трубопровод основной	—						
—	Трубопровод сбросной	—						